
عنوان پروژه: طراحی نما مســـکونی
کارفرما: جناب آقای رمضانی


Radco Deco Group

majideisapour.ir

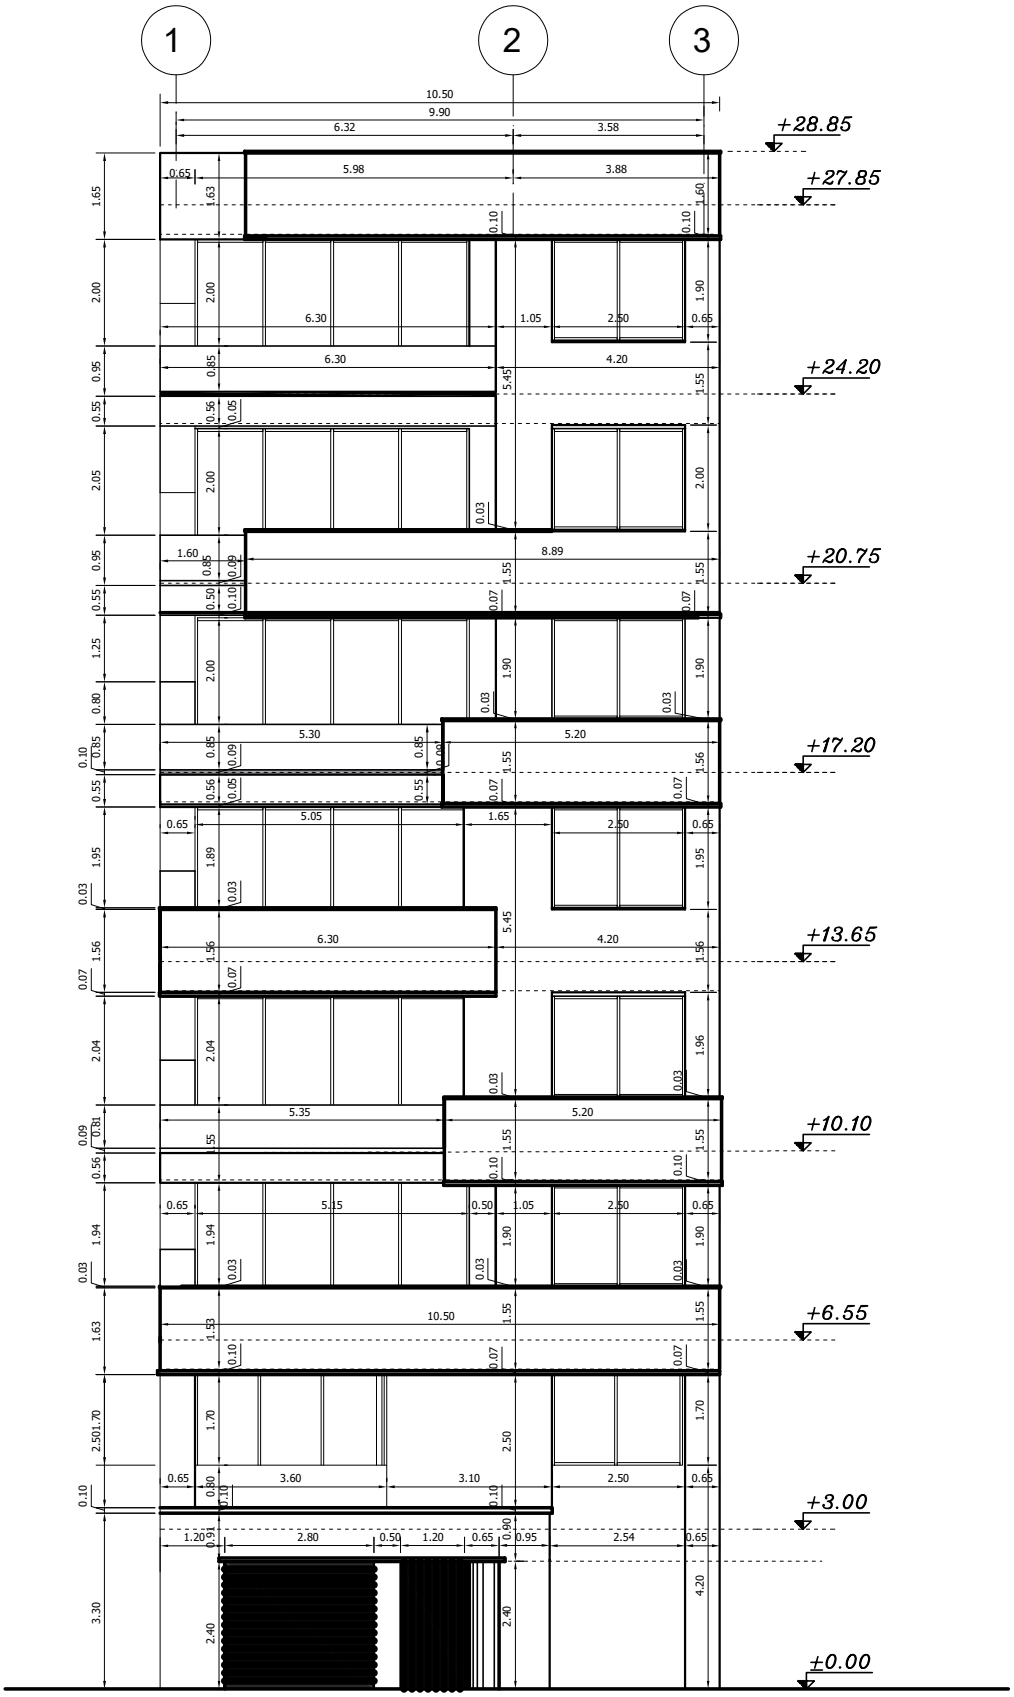


عنوان پروژه: طراحی پوسته نما جنوبی	
کار فرما: آقای رمضانی	
شماره پروژه: P-0218	MajidEisapour Building Consulting +98 911 226 5584
نوع نقشه: معماری	
عنوان نقشه: جزییات اجرایی	
شماره نقشه: A1-01	
مقیاس نقشه: 1/100	

مدیر پروژه: مهندس رمضانی	همکاران پروژه:
طراح معمار: مهندس مجید عیسی پور	
کنترل: مهندس مجید عیسی پور	
ترسیم: مهندس فاطمه رسولی	
تاریخ: 05/07/20	
آدرس پروژه:	

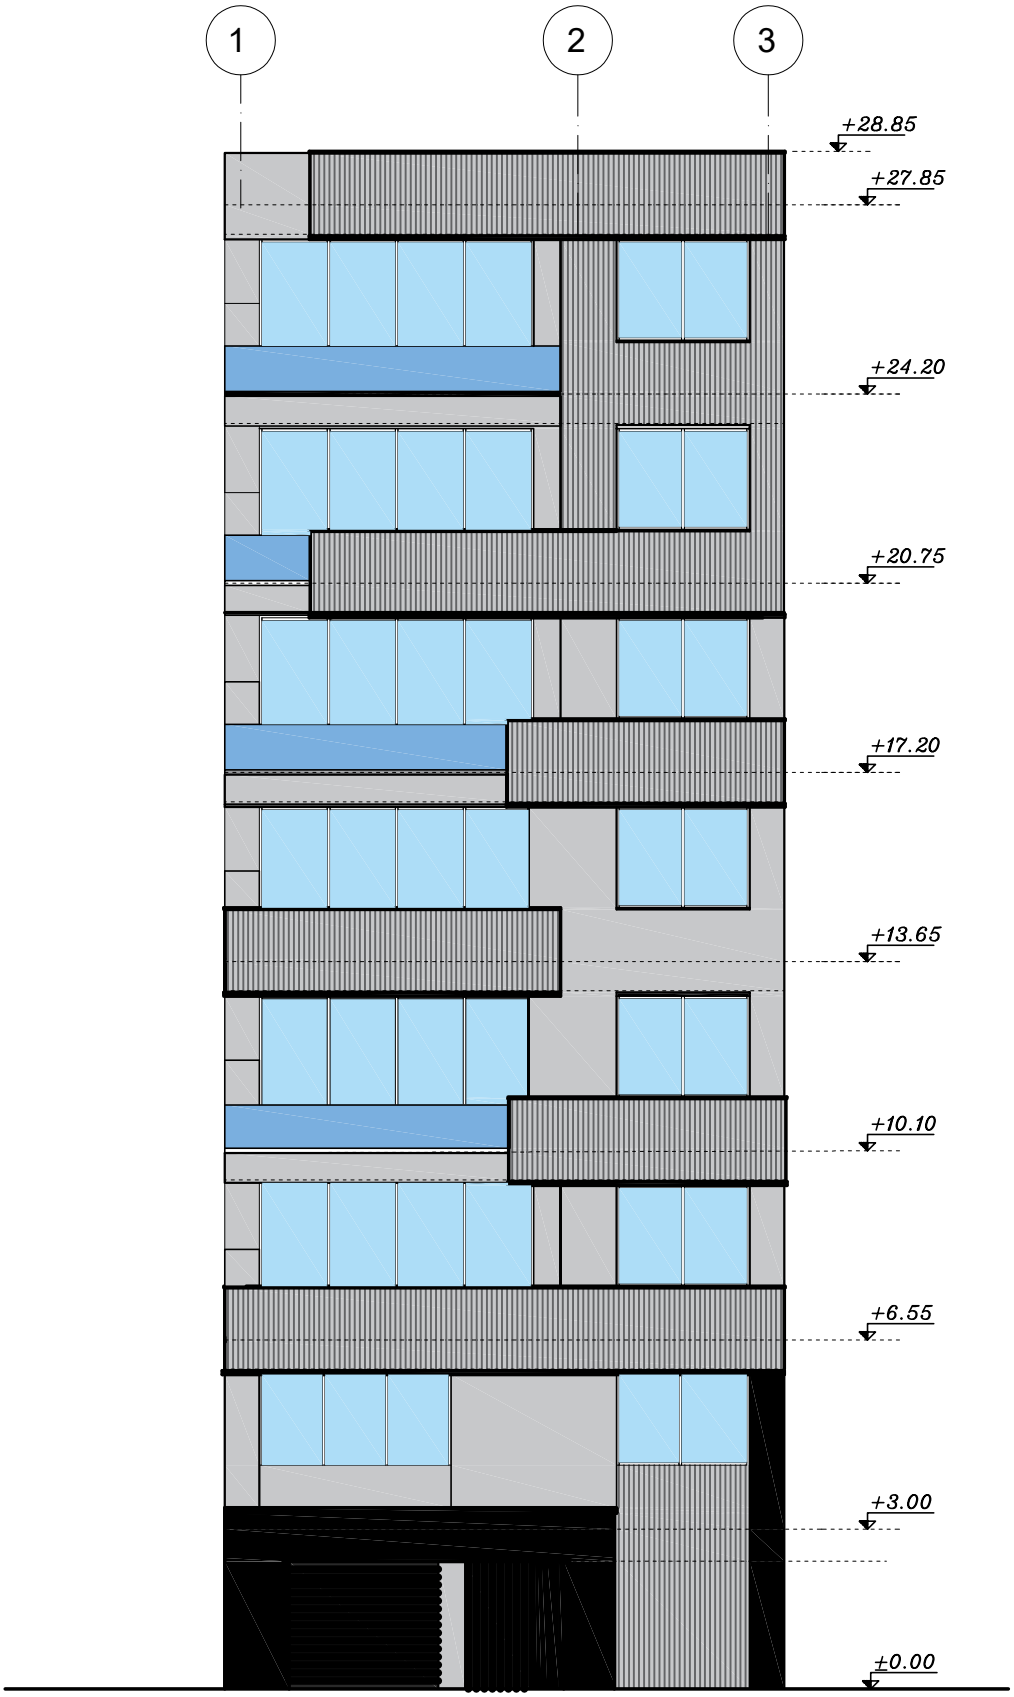

عنوان پروژه: طراحی پوسته نما جنوبی	
کار فرما: آقای رمضانی	
شماره پروژه: P-0218	MajidEisapour Building Consulting +98 911 226 5584
نوع نقشه: معماری	
عنوان نقشه: جزییات اجرایی	
شماره نقشه: A1-02	
مقیاس نقشه: 1/100	

مدیر پروژه: مهندس رمضانی	همکاران پروژه:
طراح معمار: مهندس مجید عیسی پور	
کنترل: مهندس مجید عیسی پور	
ترسیم: مهندس فاطمه رسولی	
تاریخ: 05/07/20	
آدرس پروژه:	

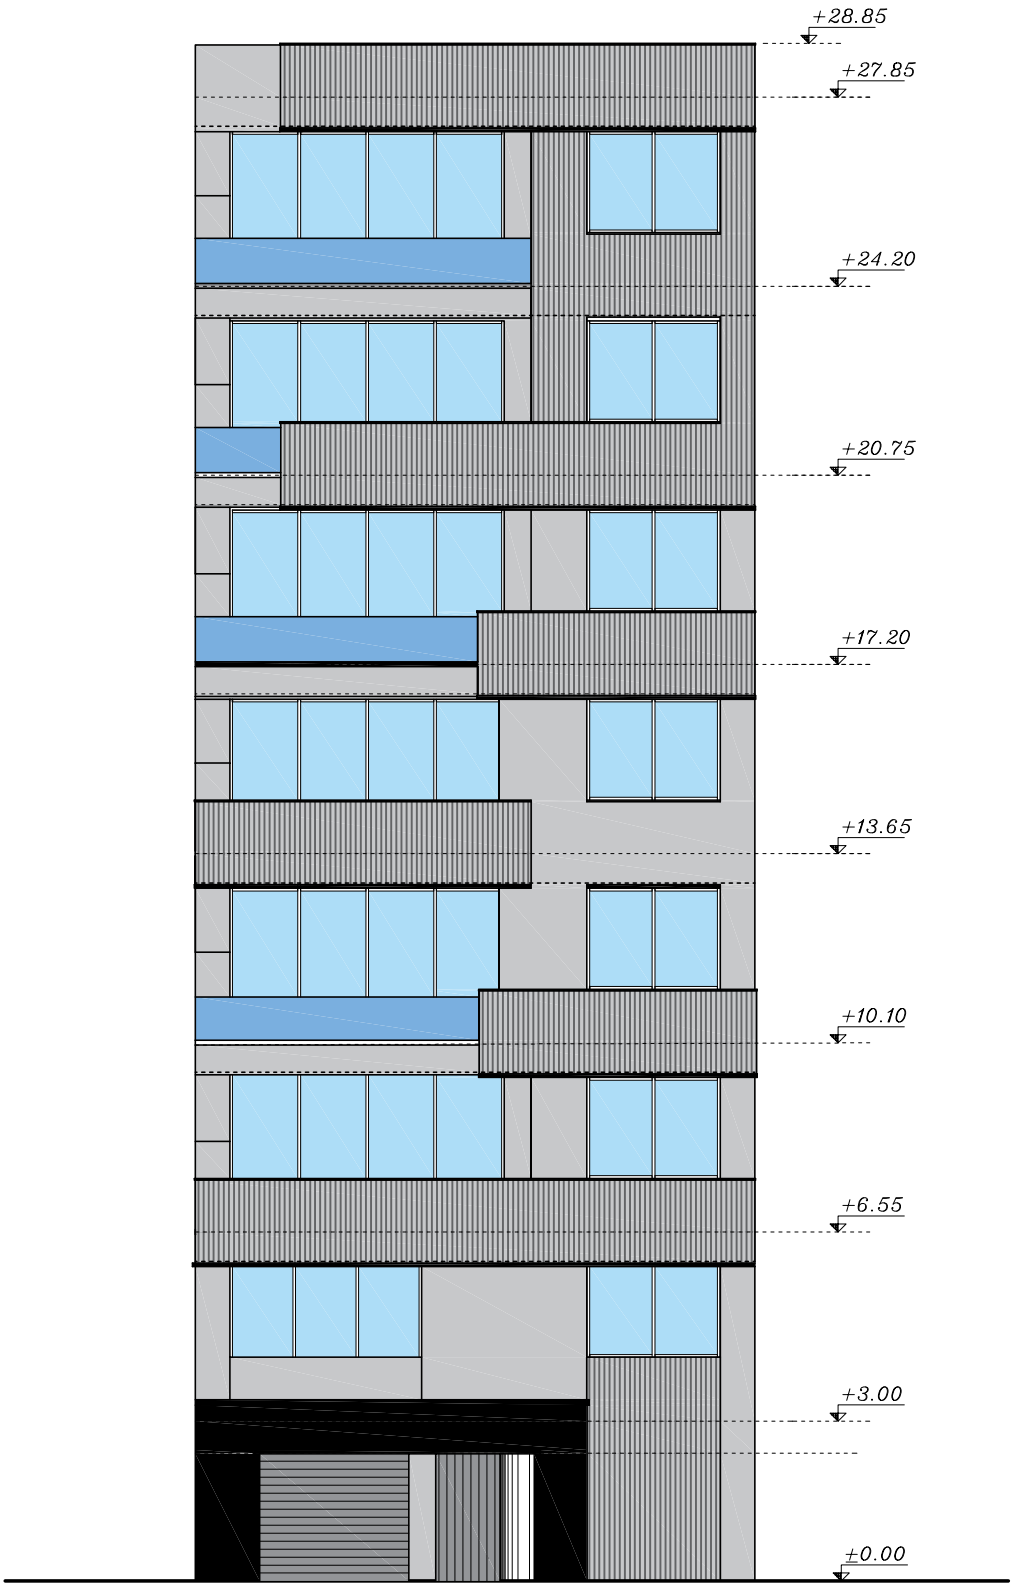

عنوان پروژه: طراحی پوسته نما جنوبی

کار فرما: آقای رمضانی

شماره پروژه: P-0218

نوع نقشه: معماری

عنوان نقشه: جزییات اجرایی

شماره نقشه: A1-03

مقیاس نقشه: 1/100

MajidEisapour
Building Consulting
+98 911 226 5584

مدیر پروژه: مهندس رمضانی

طراح معمار: مهندس مجید عیسی پور


کنترل: مهندس مجید عیسی پور

ترسیم: مهندس فاطمه رسولی

تاریخ: 05/07/20


همکاران پروژه:

آدرس پروژه:

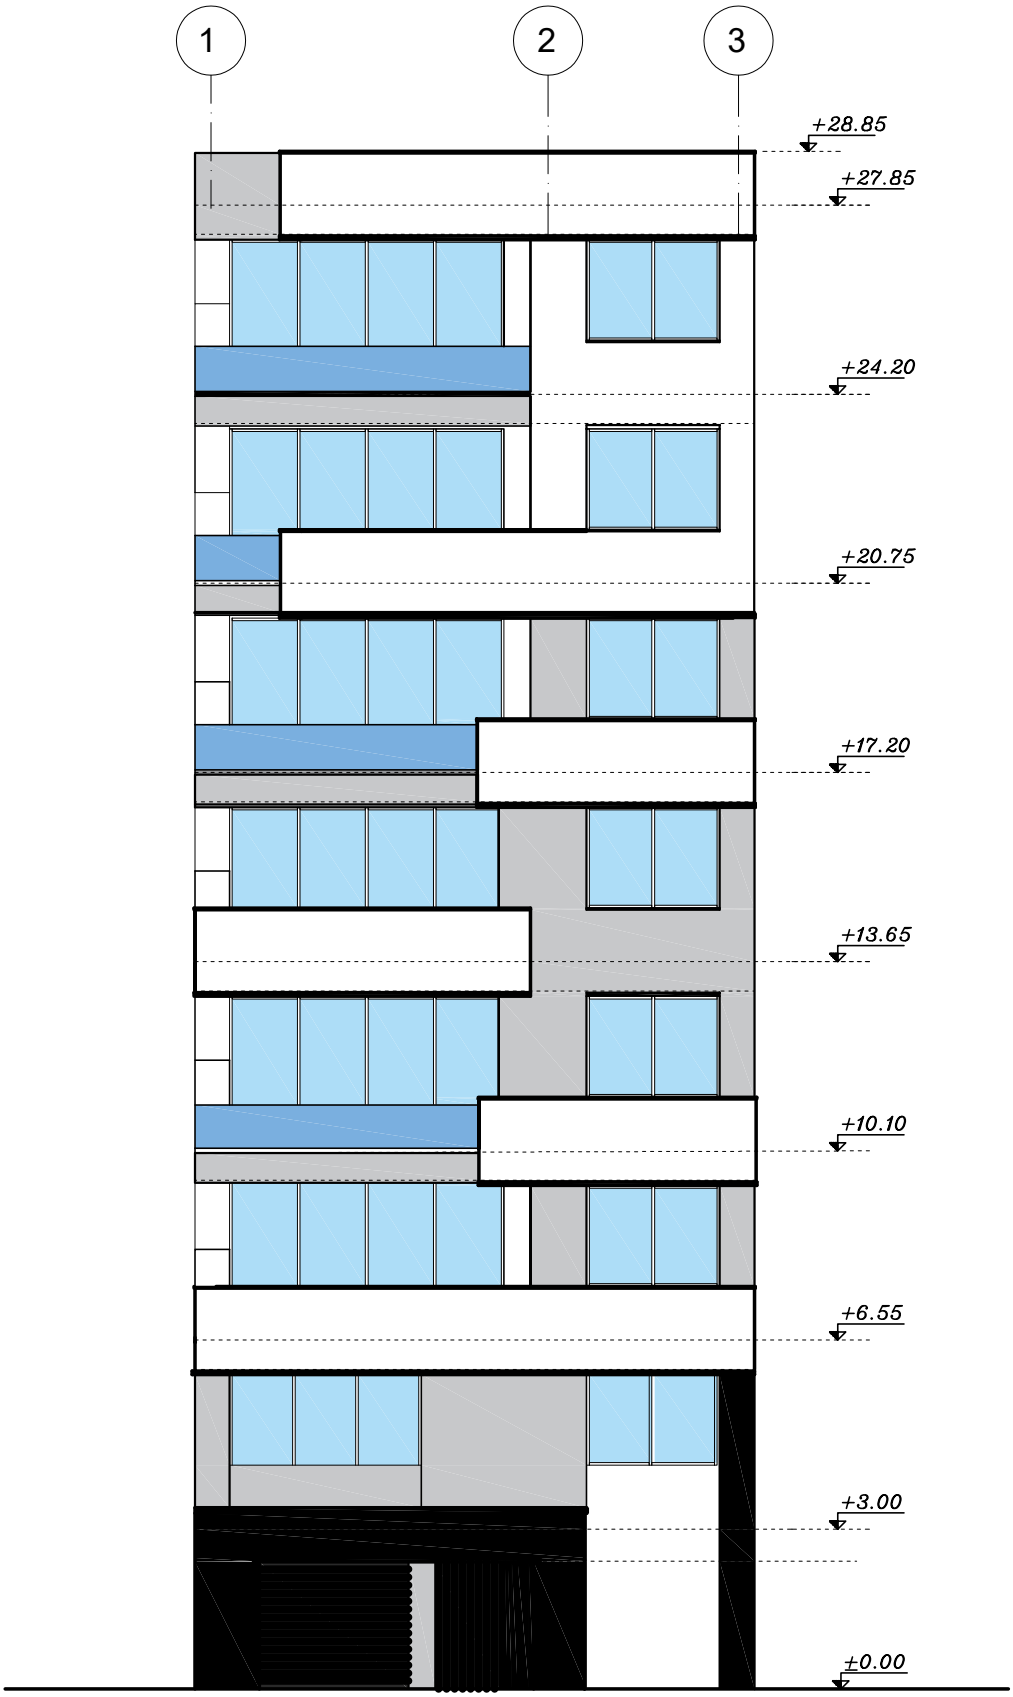

عنوان پروژه: طراحی پوسته نما جنوبی	
کار فرما: آقای رمضانی	
شماره پروژه: P-0218	MajidEisapour Building Consulting +98 911 226 5584
نوع نقشه: معماری	
عنوان نقشه: جزییات اجرایی	
شماره نقشه: A1-04	
مقیاس نقشه: 1/100	

مدیر پروژه: مهندس رمضانی	همکاران پروژه:
طراح معمار: مهندس مجید عیسی پور	
کنترل: مهندس مجید عیسی پور	
ترسیم: مهندس فاطمه رسولی	
تاریخ: 05/07/20	
آدرس پروژه:	

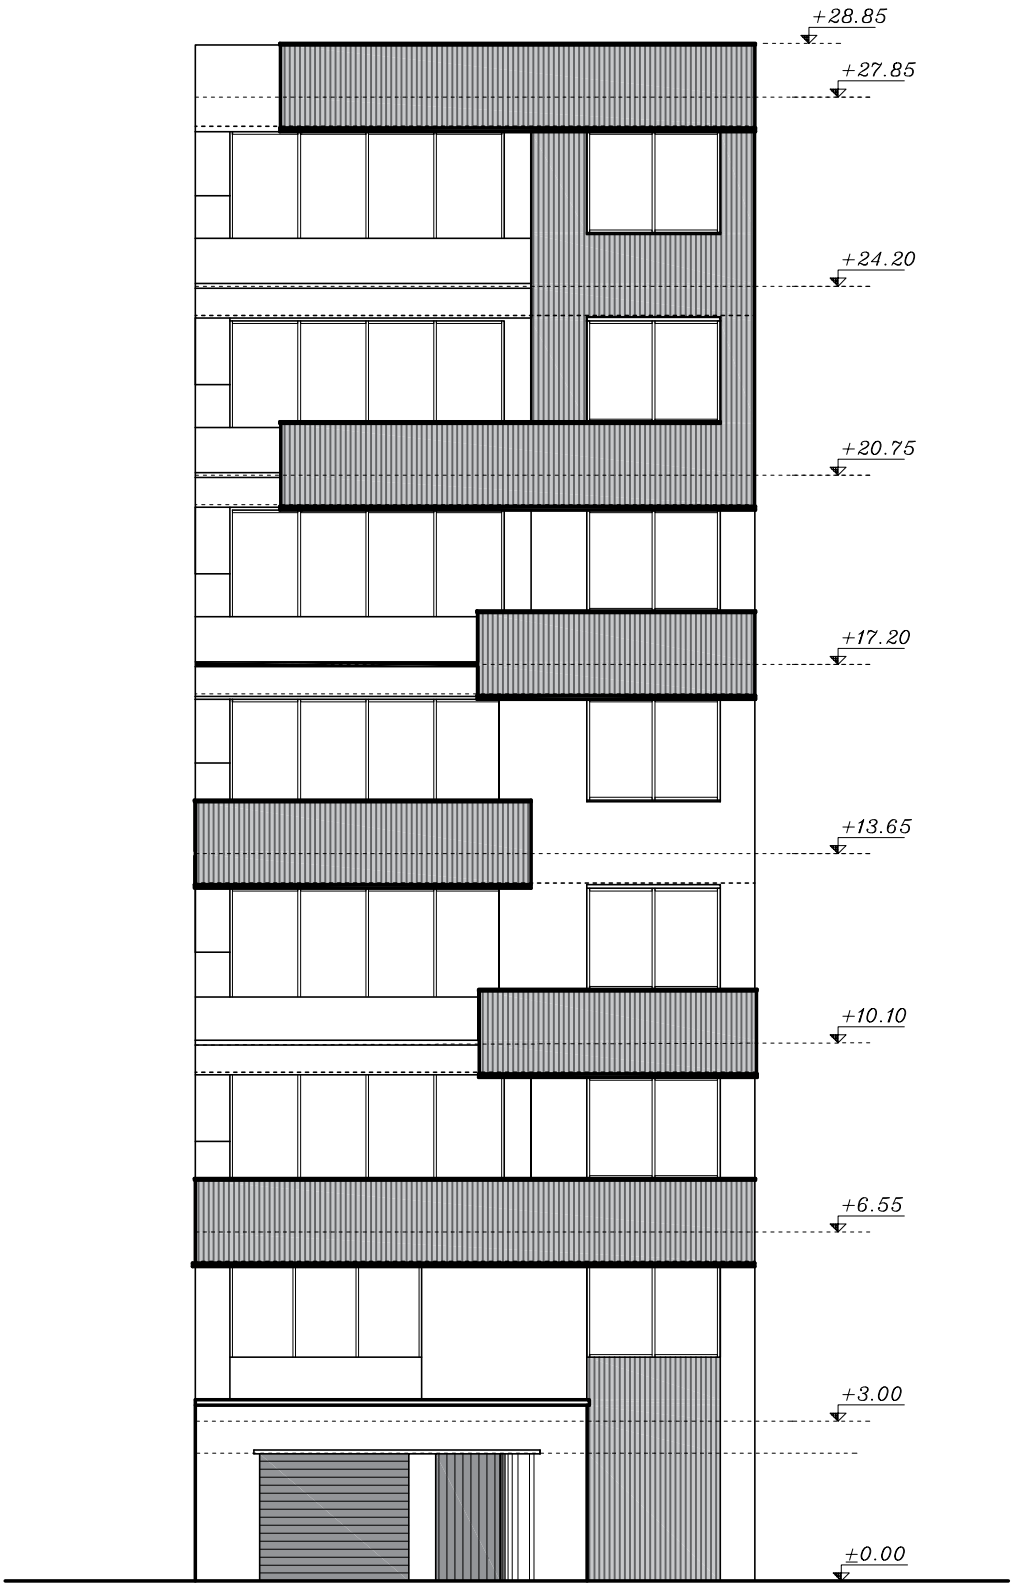

عنوان پروژه: طراحی پوسته نما جنوبی

کار فرما: آقای رمضانی

شماره پروژه: P-0218

نوع نقشه: معماری

عنوان نقشه: جزییات اجرایی

شماره نقشه: A1-05

مقیاس نقشه: 1/100

MajidEisapour
Building Consulting
+98 911 226 5584

همکاران پروژه:	
	مدیر پروژه: مهندس رمضانی
	طراح معمار: مهندس مجید عیسی پور
	کنترل: مهندس مجید عیسی پور
	ترسیم: مهندس فاطمه رسولی
	تاریخ: 05/07/20

آدرس پروژه:



عنوان پروژه: طراحی پوسته نما جنوبی

کار فرما: آقای رمضانی

شماره پروژه: P-0218

نوع نقشه: معماری

عنوان نقشه: جزییات اجرایی

شماره نقشه: A1-06

مقیاس نقشه: 1/100

MajidEisapour
Building Consulting
+98 911 226 5584

مدیر پروژه: مهندس رمضانی

طراح معمار: مهندس مجید عیسی پور

کنترل: مهندس مجید عیسی پور

ترسیم: مهندس فاطمه رسولی

تاریخ: 05/07/20

همکاران پروژه:

آدرس پروژه: